


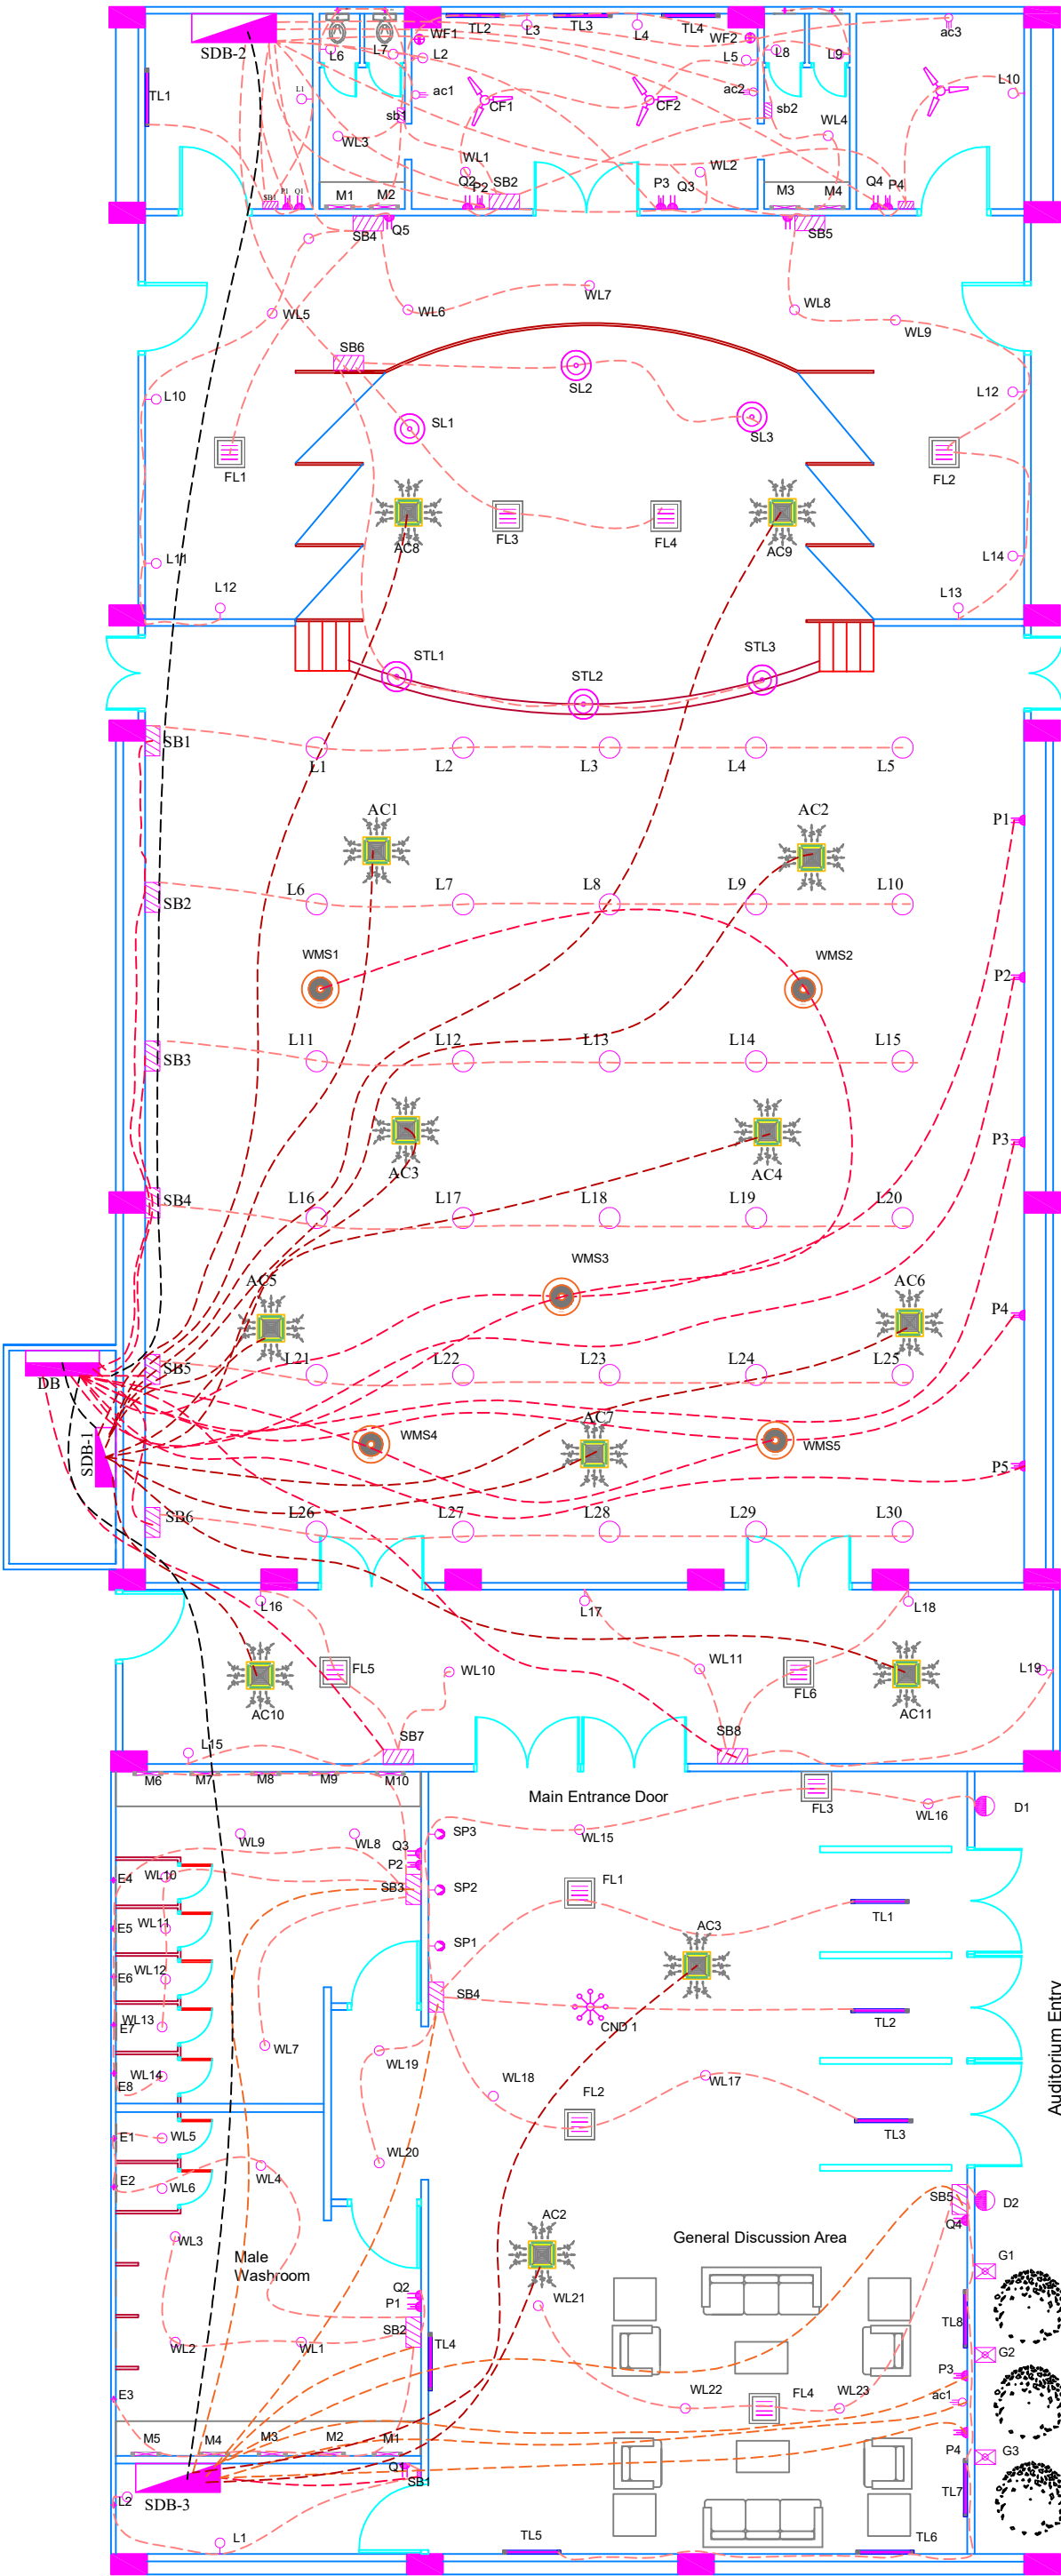

ELECTRICAL LEGEND

ICON	Name
	SDB (Sub Distribution board)
	DB (Distribution board)
	SB (Switch board)
	Ceiling Fan (CF)
	Wall bracket light (WL)
	Tube light (TL)
	Mirror light (M)
	Stage Light(StL)/Stage Spot Light(SL)
	Garden light (G)
	Door Light(D)
	Wall Fan (WF)
	Ceiling light (CL)
	15A/16A 3 Pin Switched socket AC(ac)
	5A/10A 2 Pin switched socket (Q)
	5A/10A 3 Pin switched socket(P)
	Exhaust Fan (E)
	Flat LED Light (FL)
	Exhibition Spot Light (SP)
	Central AC (AC)
	Wall Mounted Speaker (WMS)

CABLE SCHEDULE

- ↯C7 = 1- C, 4x2.5 mm2 (BYA) Cable + 2x1.5 (re) mm2 E.C.C
- ↯C15 = 4x 1C X 10.0 Sq.mm NYY / BYA + 6.0 Sq. mm ECC
- ↯C16 = 4x 1C x 16.0 Sq.mm NYY / BYA + 10.0 Sq. mm ECC

Student's Information

ID	NAME
202216049	Raisul Islam Ratul
202216051	Rakibul Hasan Rakib
202216053	Sadman A Rahman

Group-A9
Auditorium